


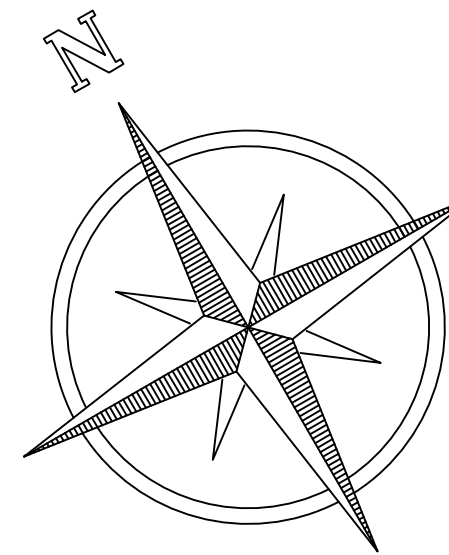

ALL UNITS IN METER

- CW RISER
- HW RISER
- ⚡ GATE VALVE
- HW SUPPLY
- CW SUPPLY

Design Studio (10), Technical
Project, 2025/2026

INSTRUCTORS:
Prof. Othman Alshamrani (Co)
Prof. Mohammed Essam Shaawat
Dr. M. Abdul Mujeebu
Dr. Mohammad Farooqi
Dr. Saiful Islam
Dr. Abdulaziz Almohassen
Dr. Mohammed Alkhater
Dr. Musaad Al-hawas
Dr. Fahad Alyami
Dr. Hany Hassam Eldien
Dr. Abdullah Qahtani
Engr. Noman Ashraf
Engr. Meqdad Hasan
Engr. Rehan Jamil


DONE BY:
ABDULELAH ALQABBANI

PROJECT:
Emergency Hospital

DRAWING NAME:
supply isometric & riser


SCALE:

SHEET NUMBER:
A52

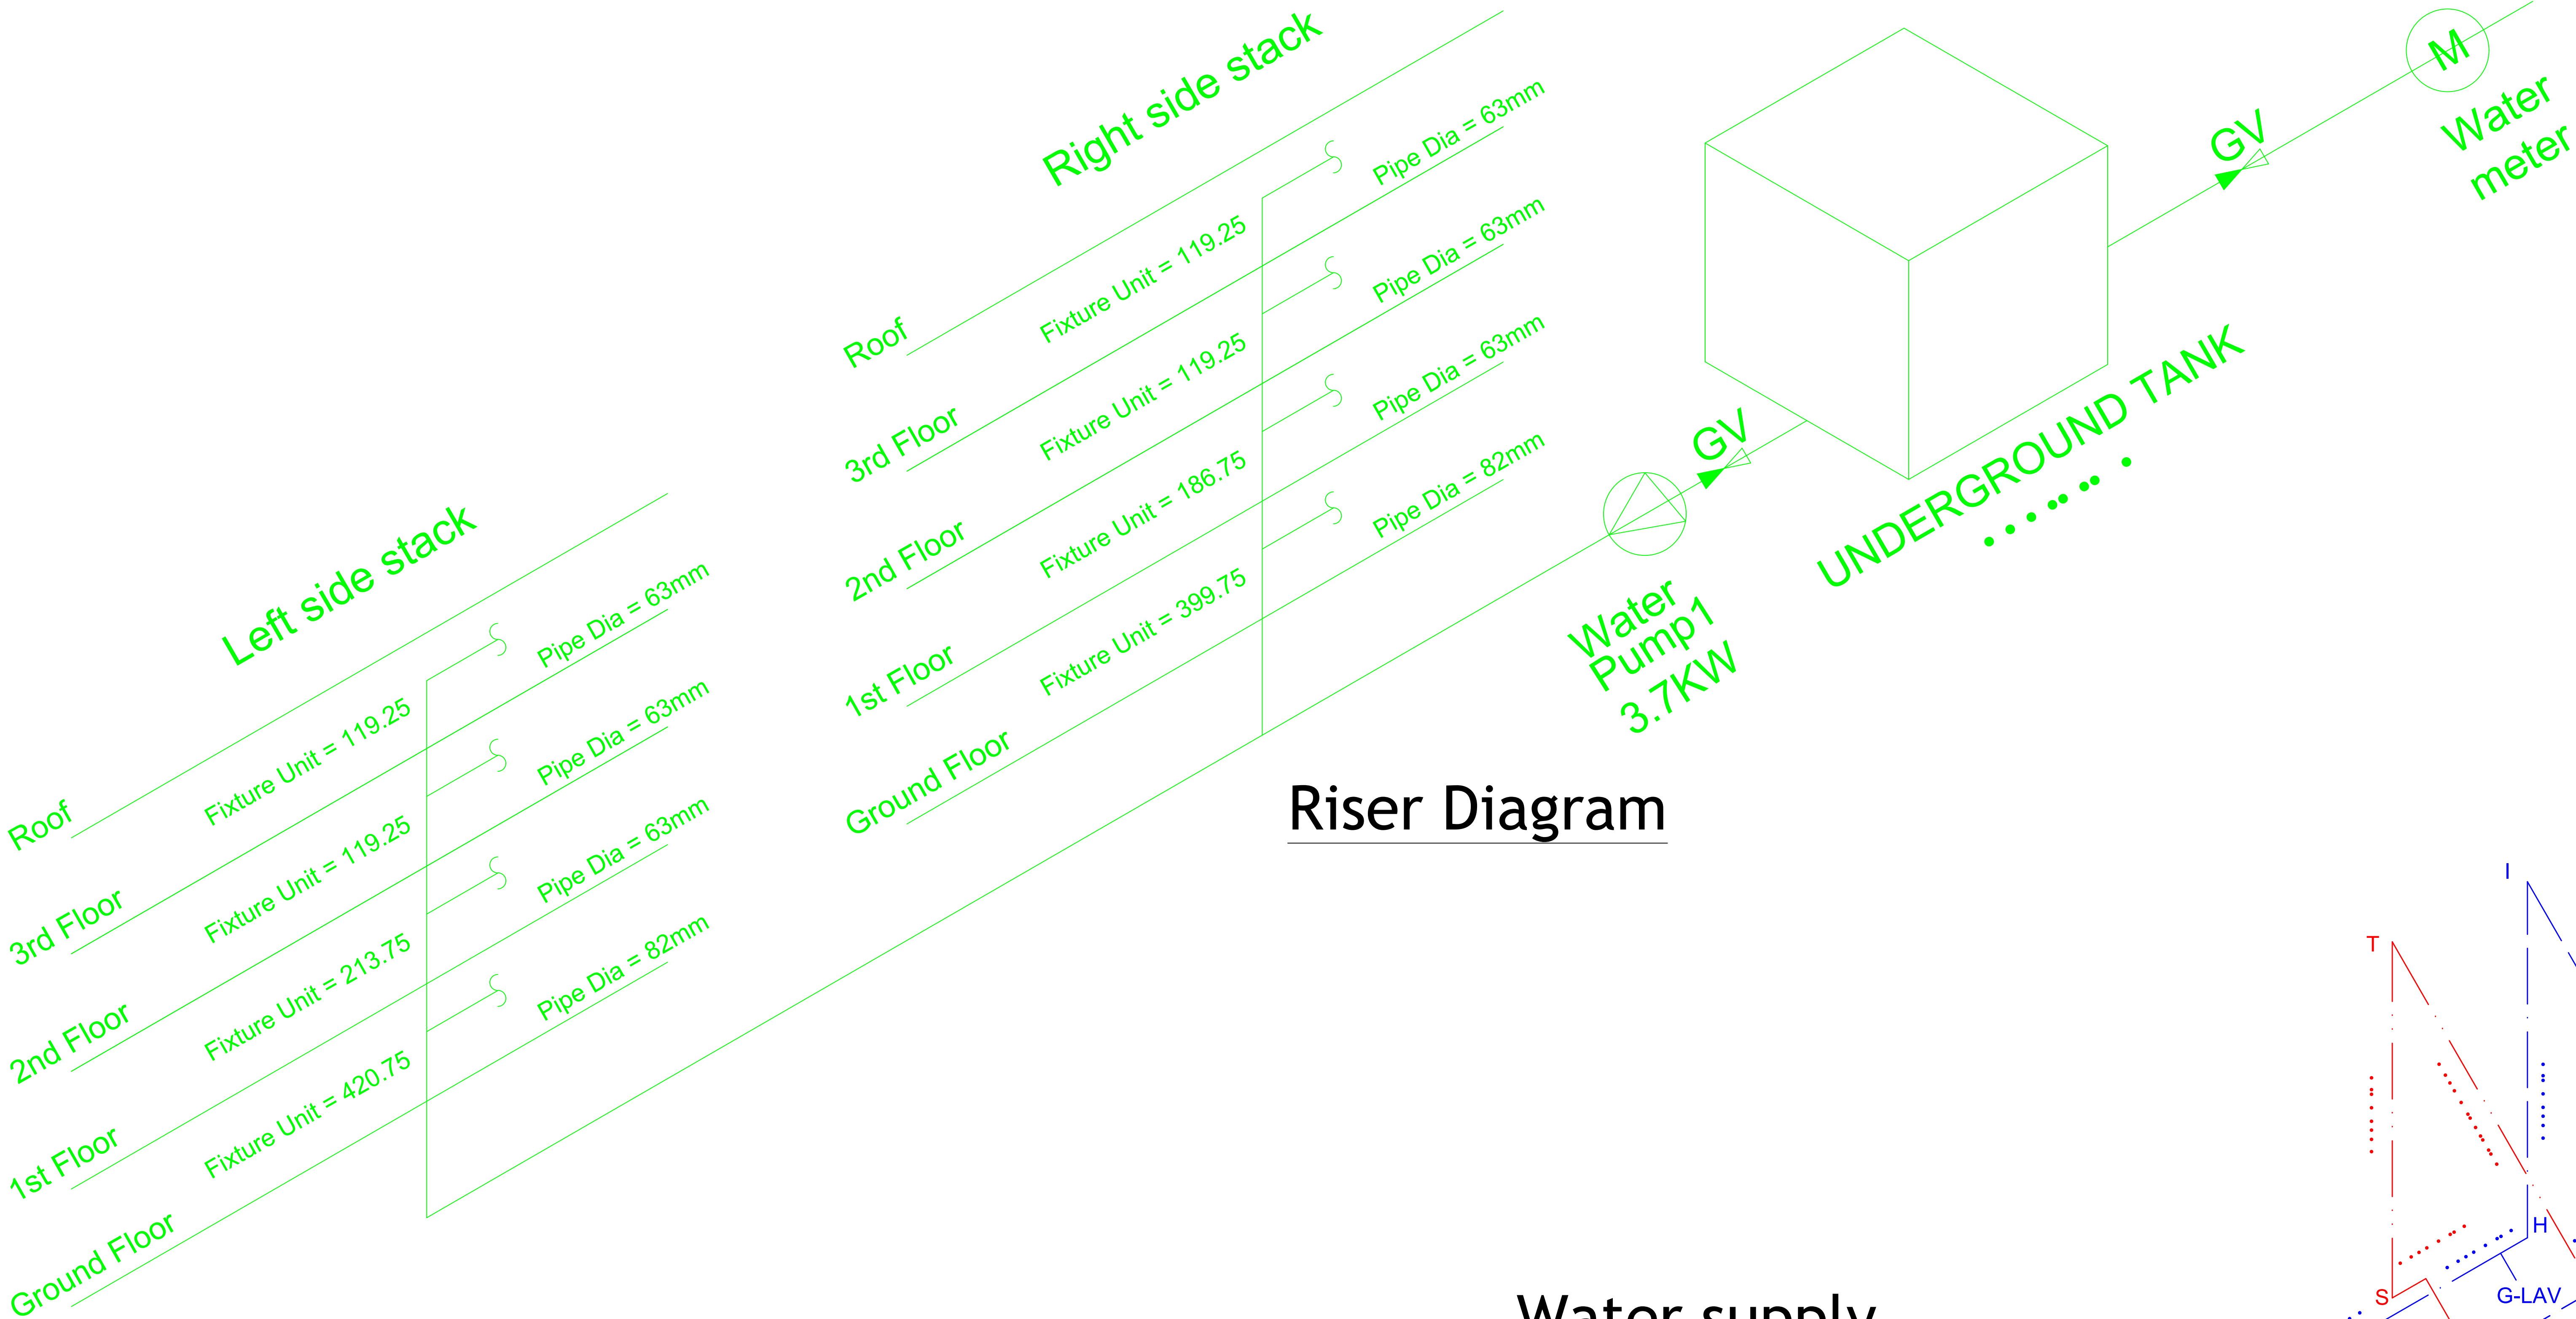

Riser Diagram

Water supply
Isometric 1:20

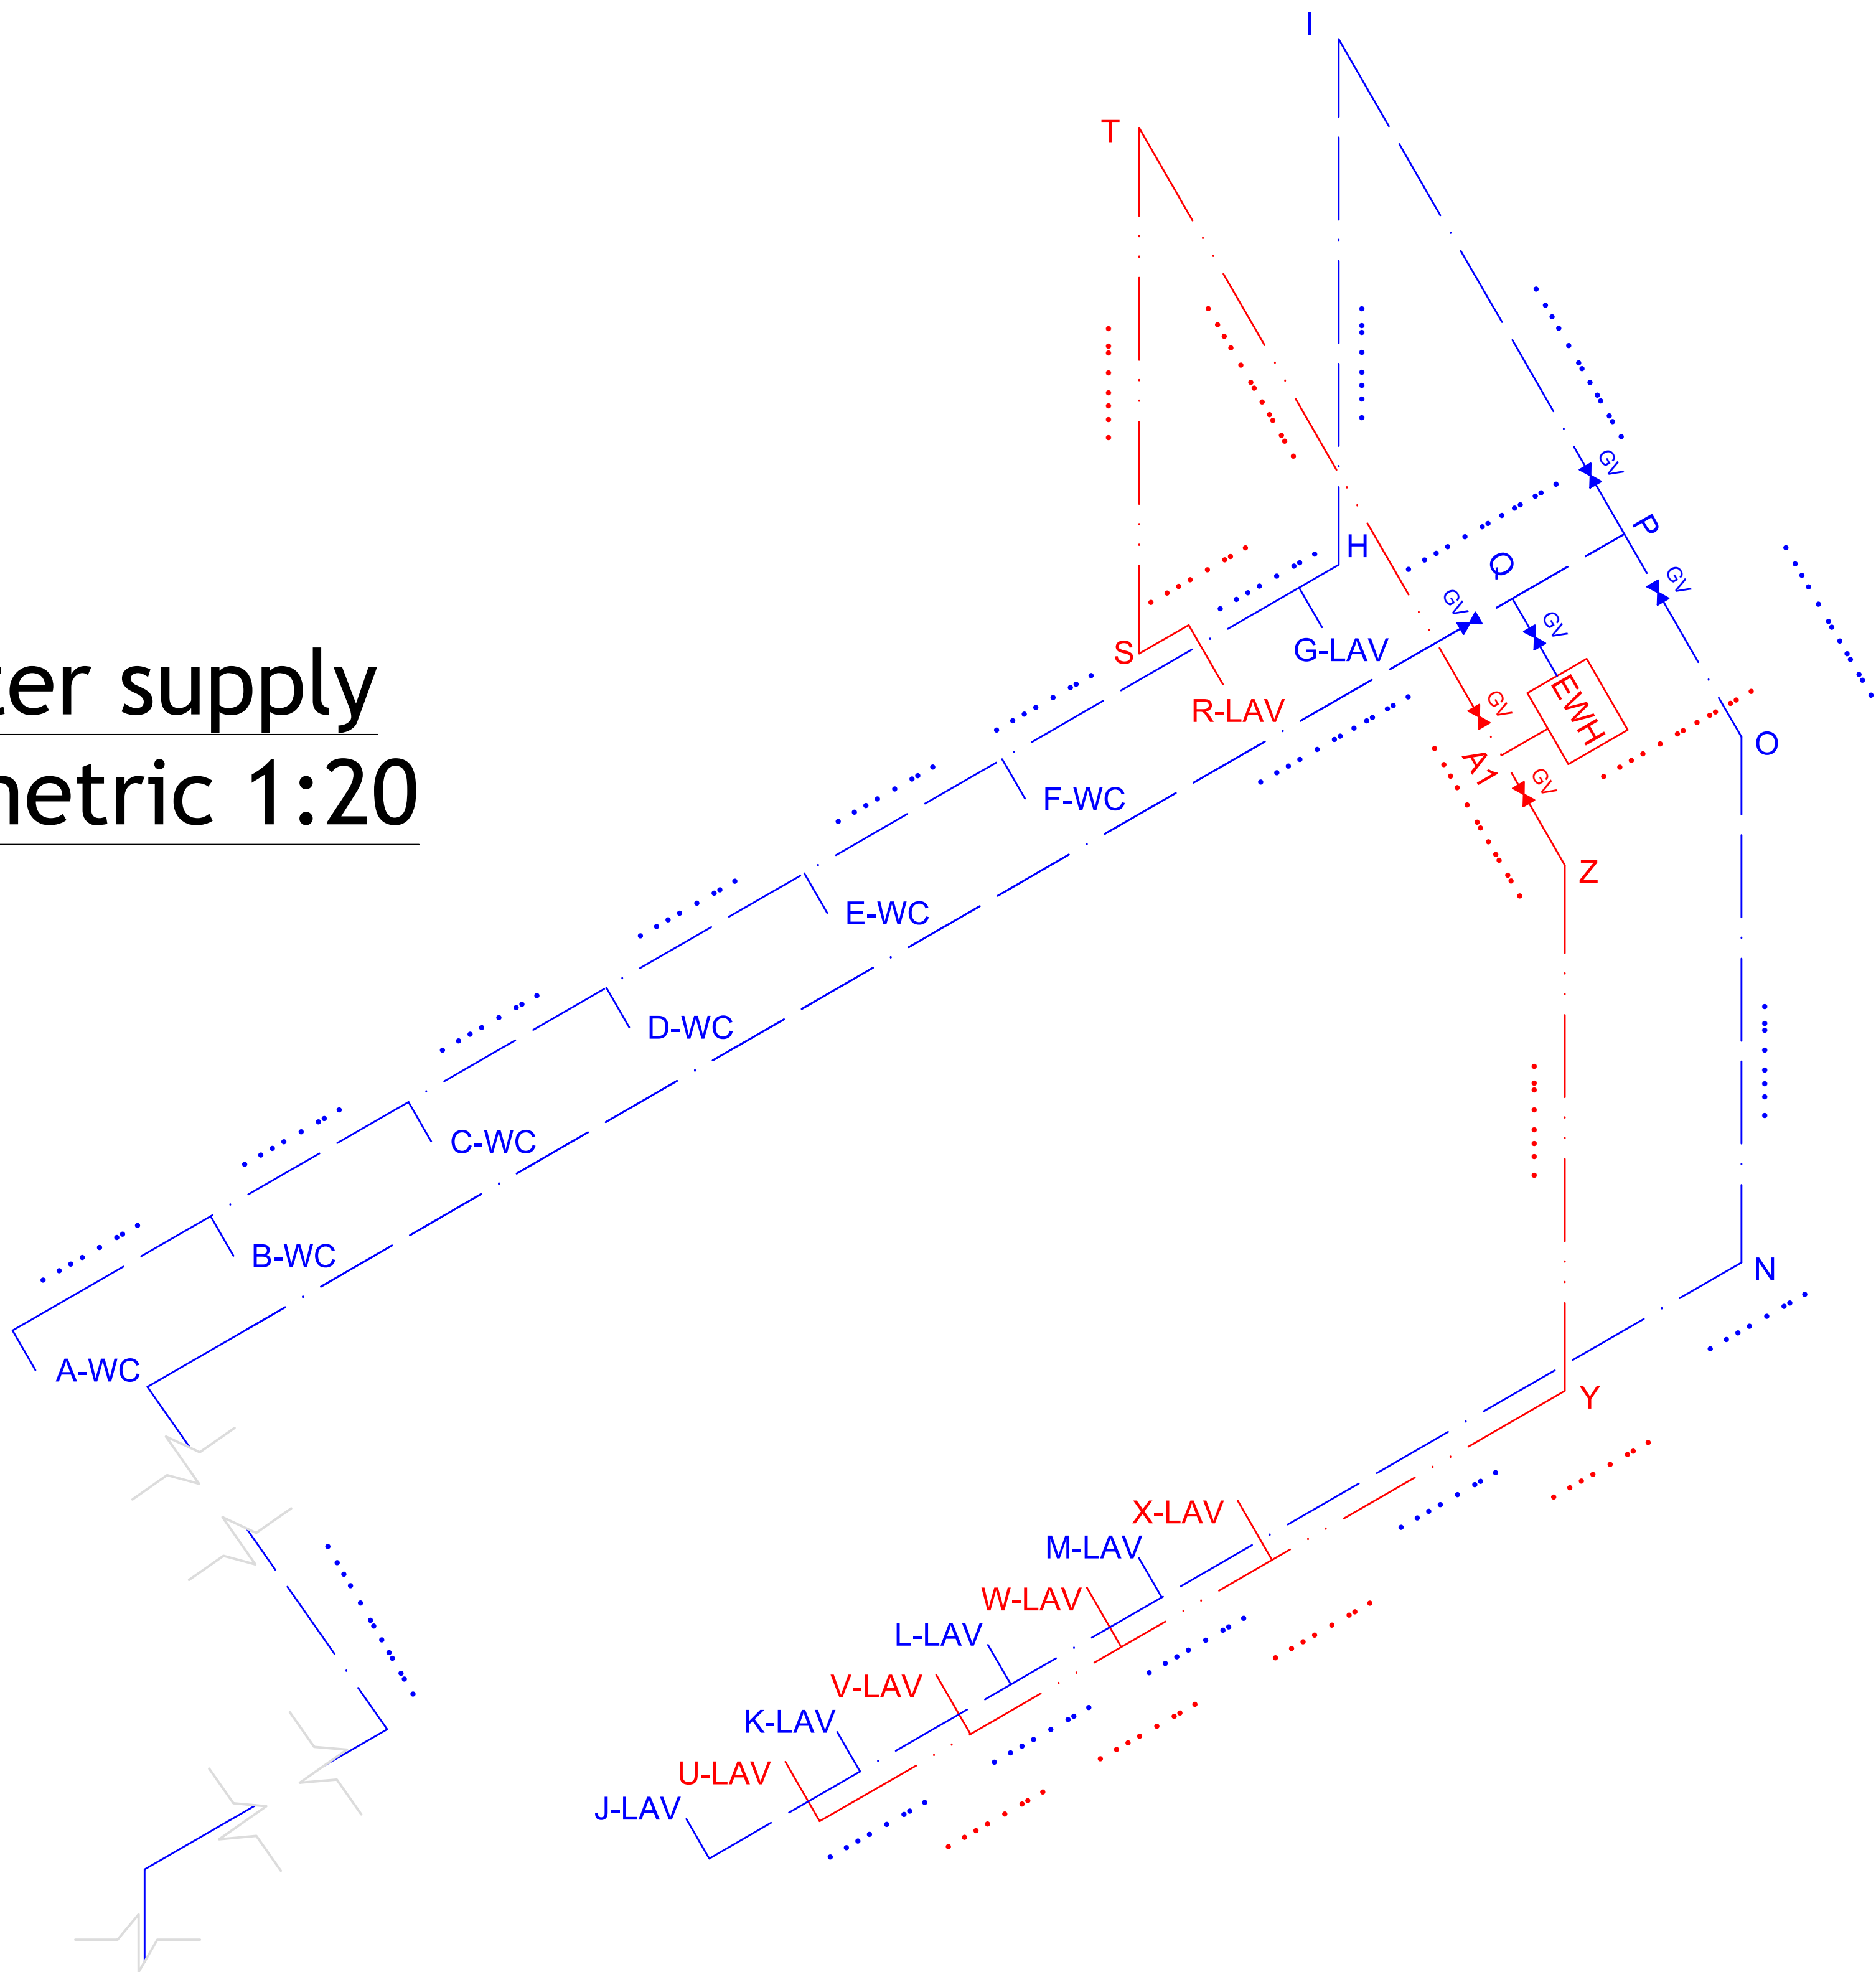

CALCULATION FOR PIPE SIZE (LEFT)					1 gpm = 0.000063 m ³ /s
pipe	Total Fixture Units	flow Q (gpm)	flow Q (m3/s)	Calculated Diameter	Selected Diameter
3F	119.25	47.83125	0.00301	50.588	63
2F	119.25+0=119.25	47.83125	0.00301	50.588	63
1F	119.25+94.5=213.75	67.75	0.00427	60.207	63
GF	213.75+207=420.75	108.9425	0.00686	76.346	82
CALCULATION FOR PIPE SIZE (RIGHT)					1 gpm = 0.000063 m ³ /s
pipe	Total Fixture Units	flow Q (gpm)	flow Q (m3/s)	Calculated Diameter	Selected Diameter
3F	119.25	47.83125	0.00301	50.588	63
2F	119.25+0=119.25	47.83125	0.00301	50.588	63
1F	119.25+67.5=186.75	62.35	0.00393	57.757	63
GF	119.25+213=399.75	104.95	0.00661	74.934	82