




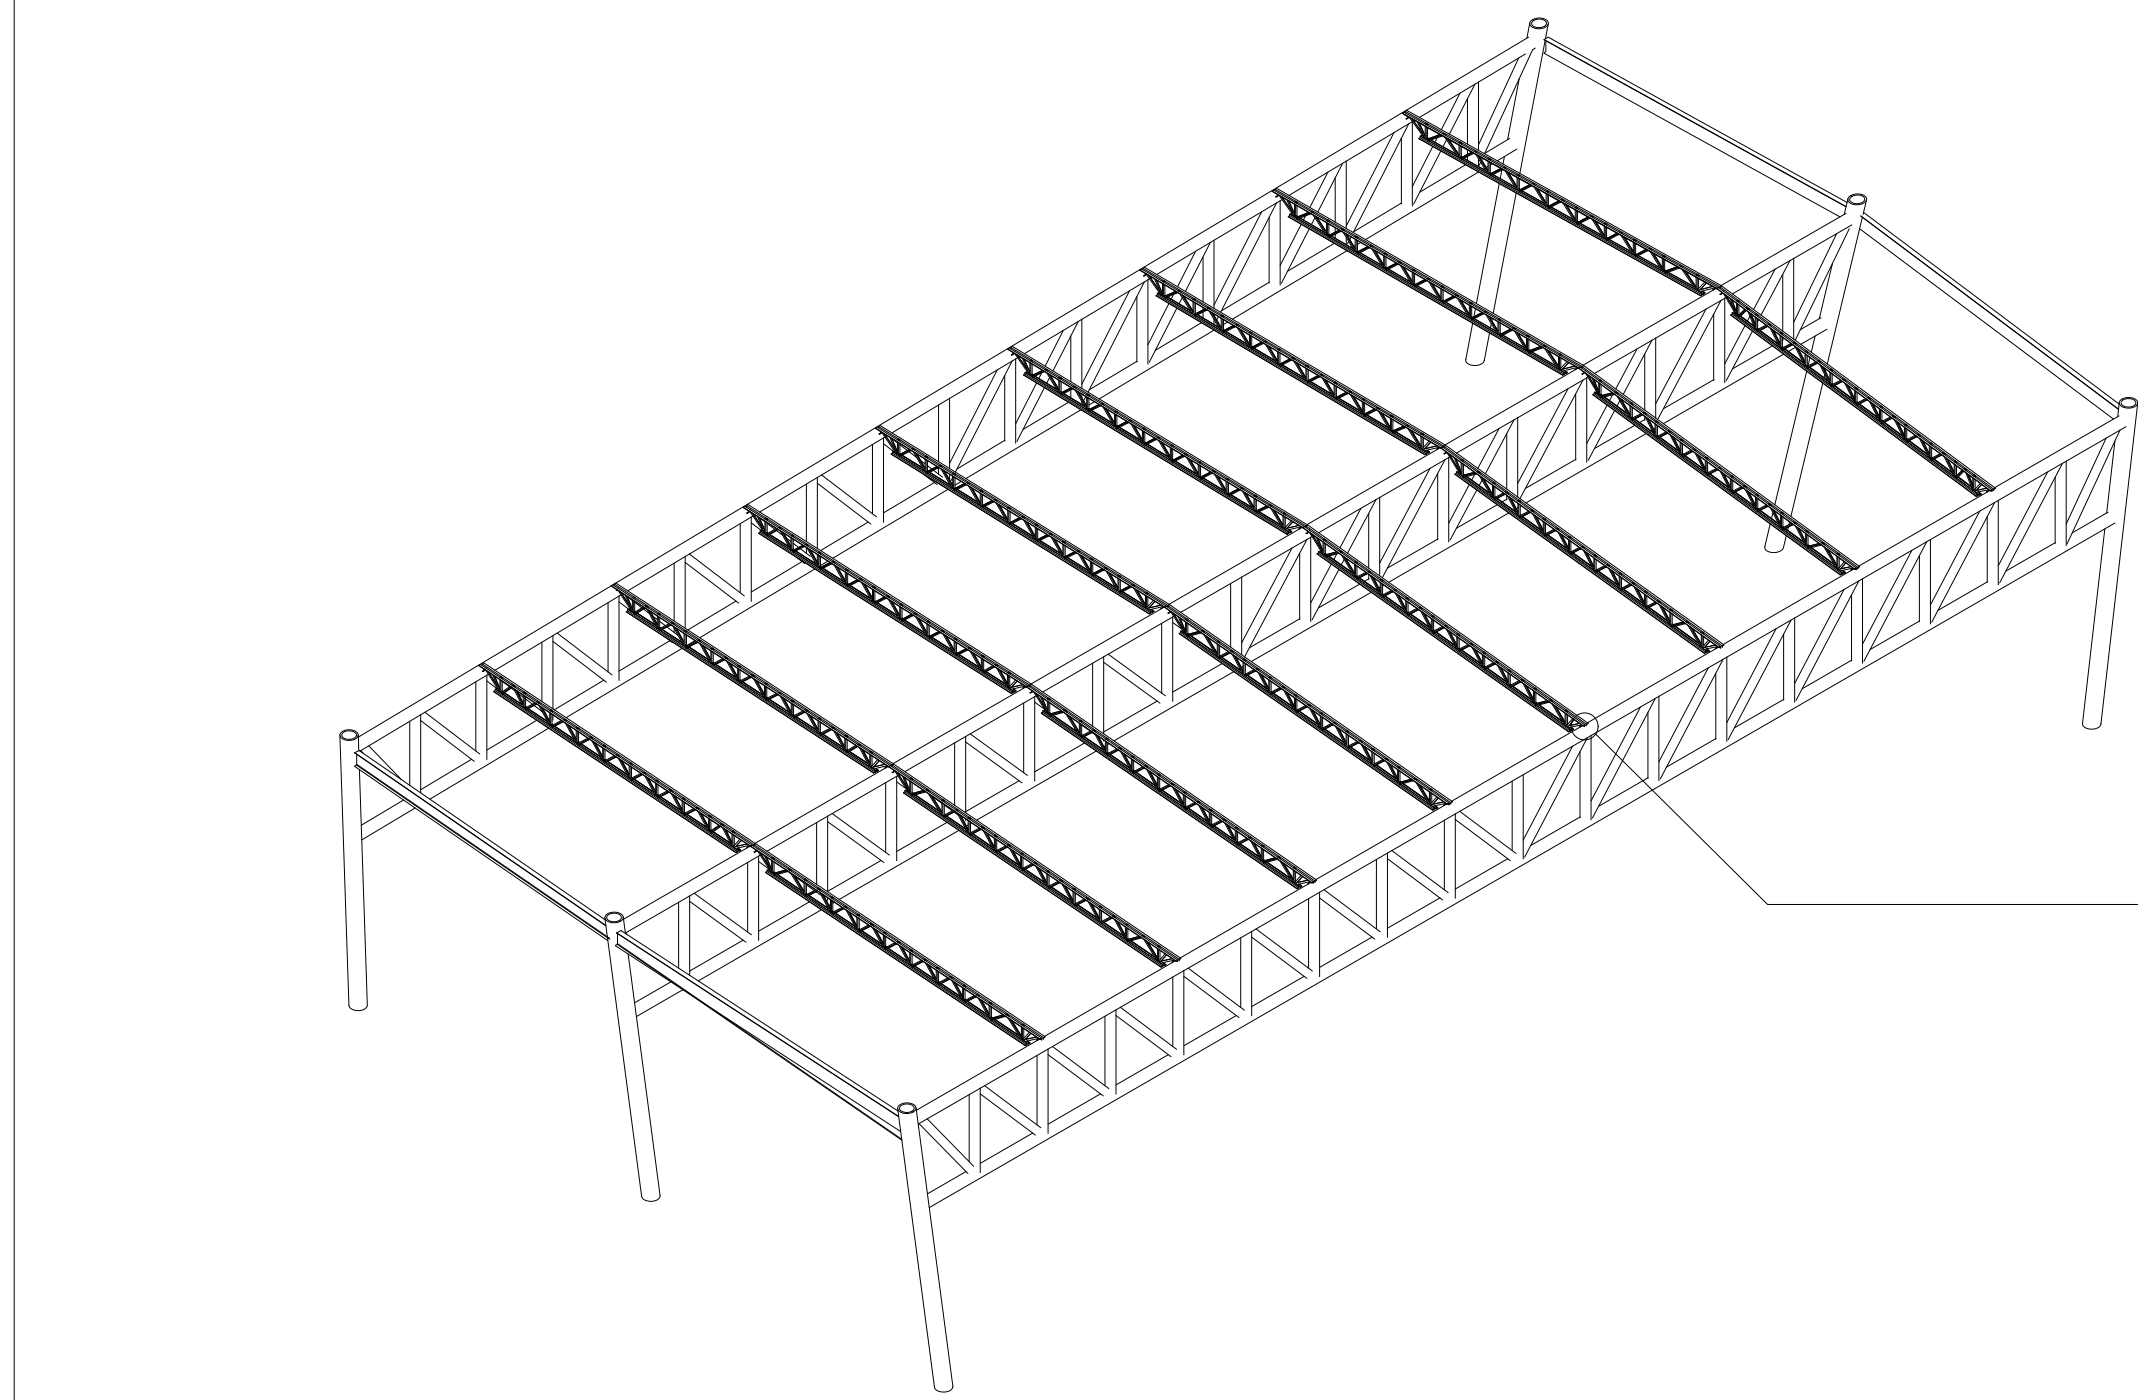


ISOLATED 3D VIEW 1 : TRUSS

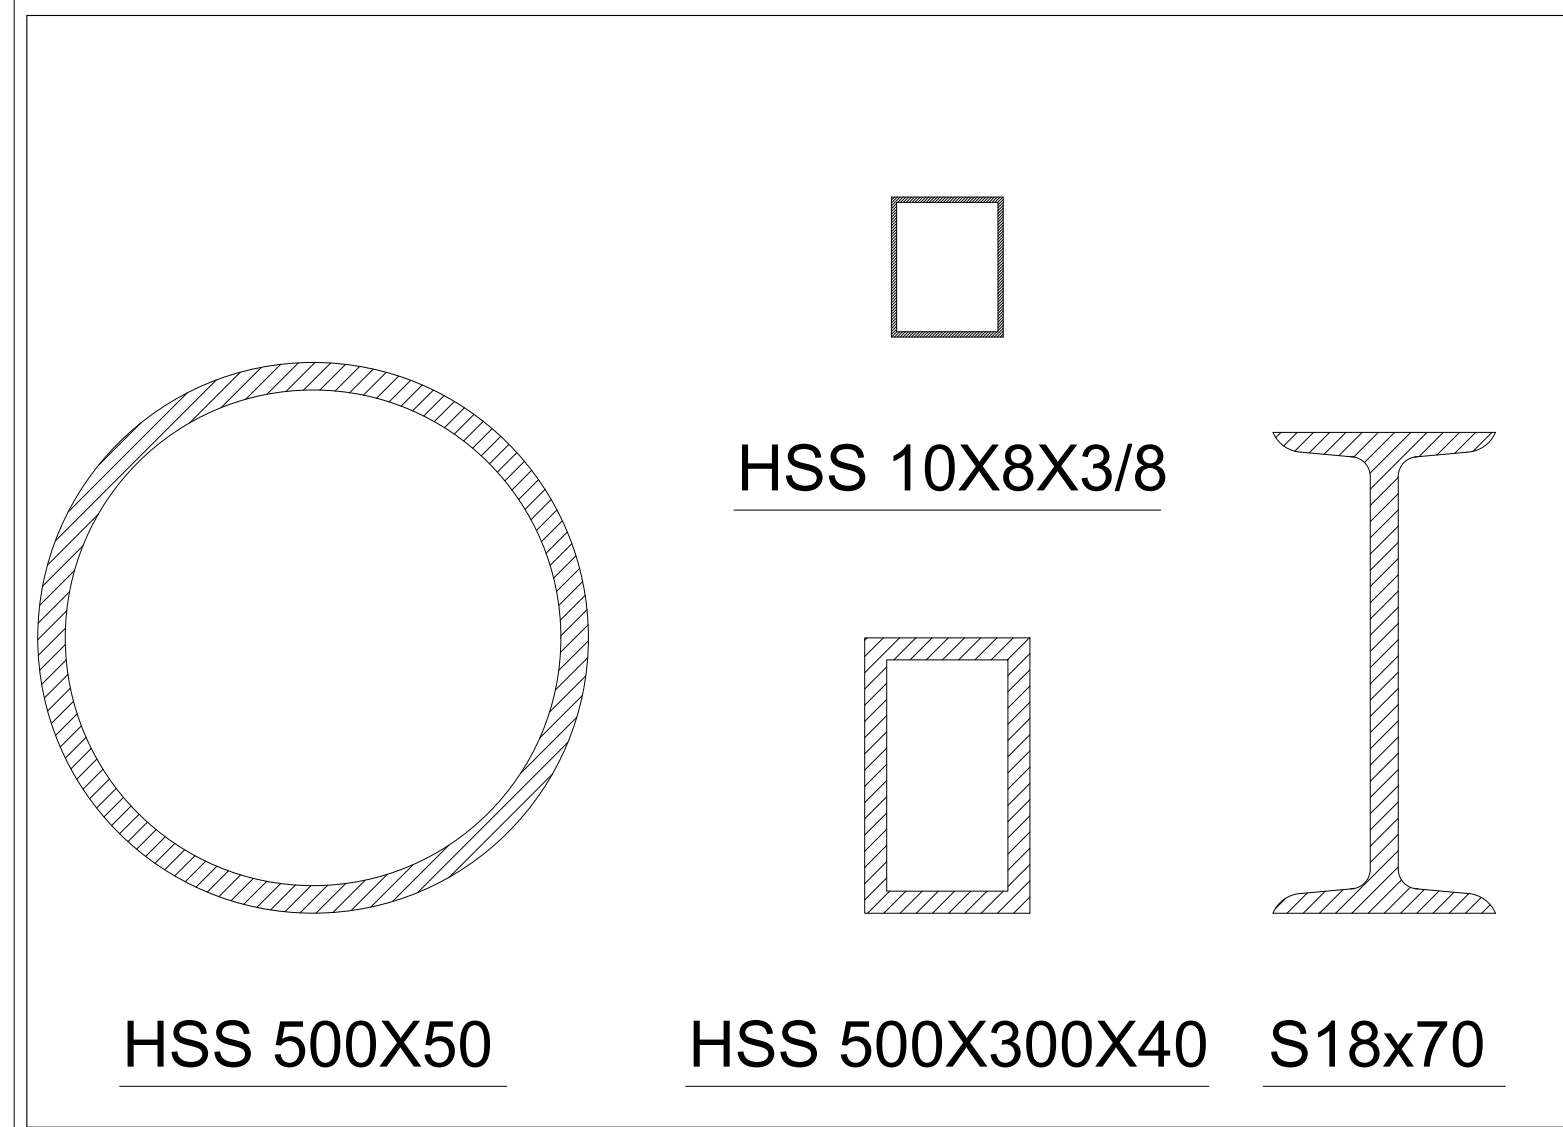

SPACE FRAME 4.8X4.8 GRID 4m DEPTH

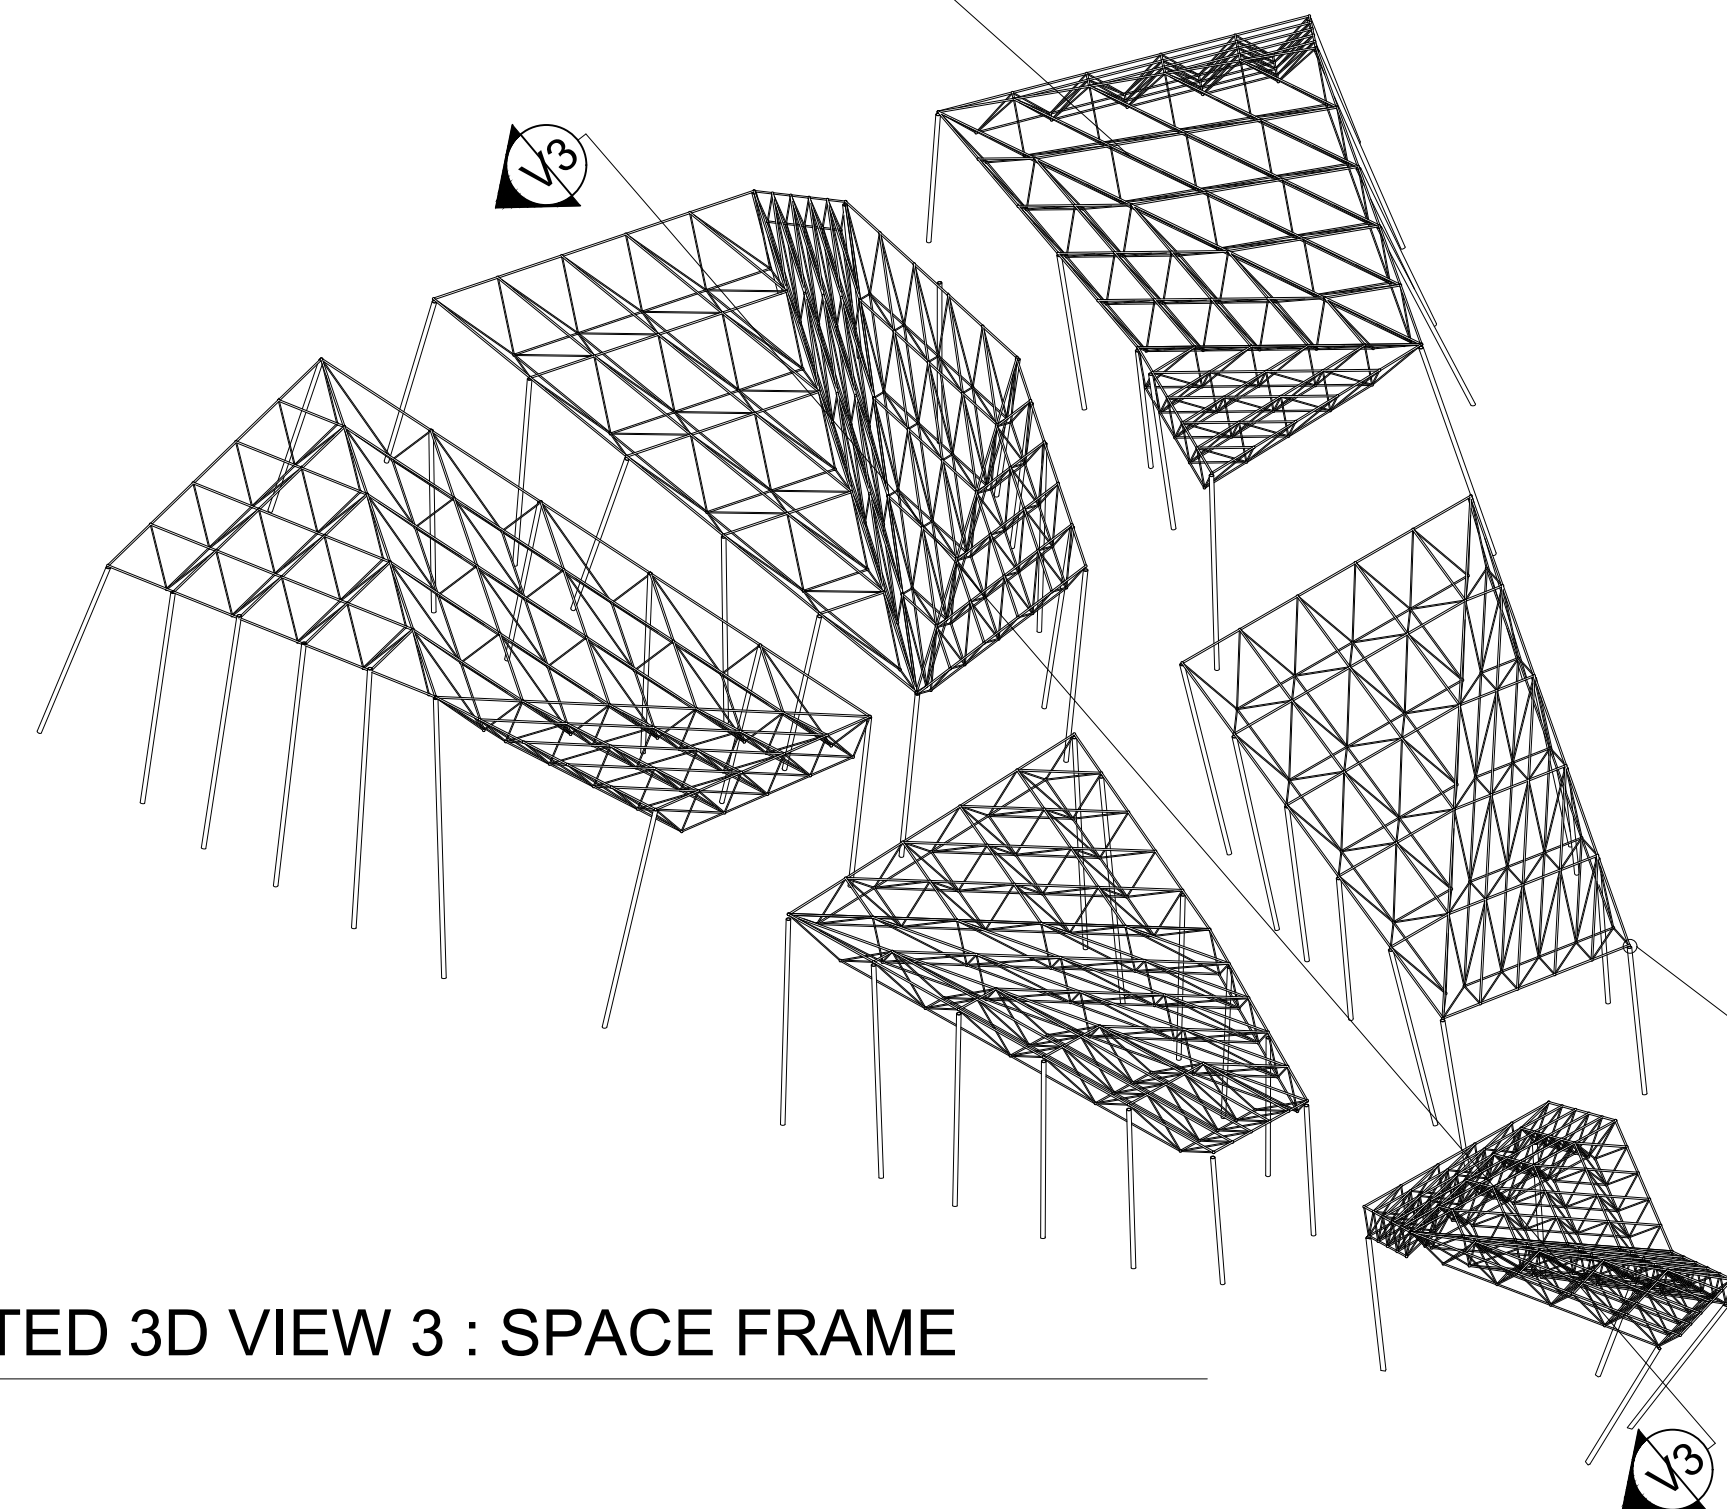


ISOLATED 3D VIEW 3 : SPACE FRAME

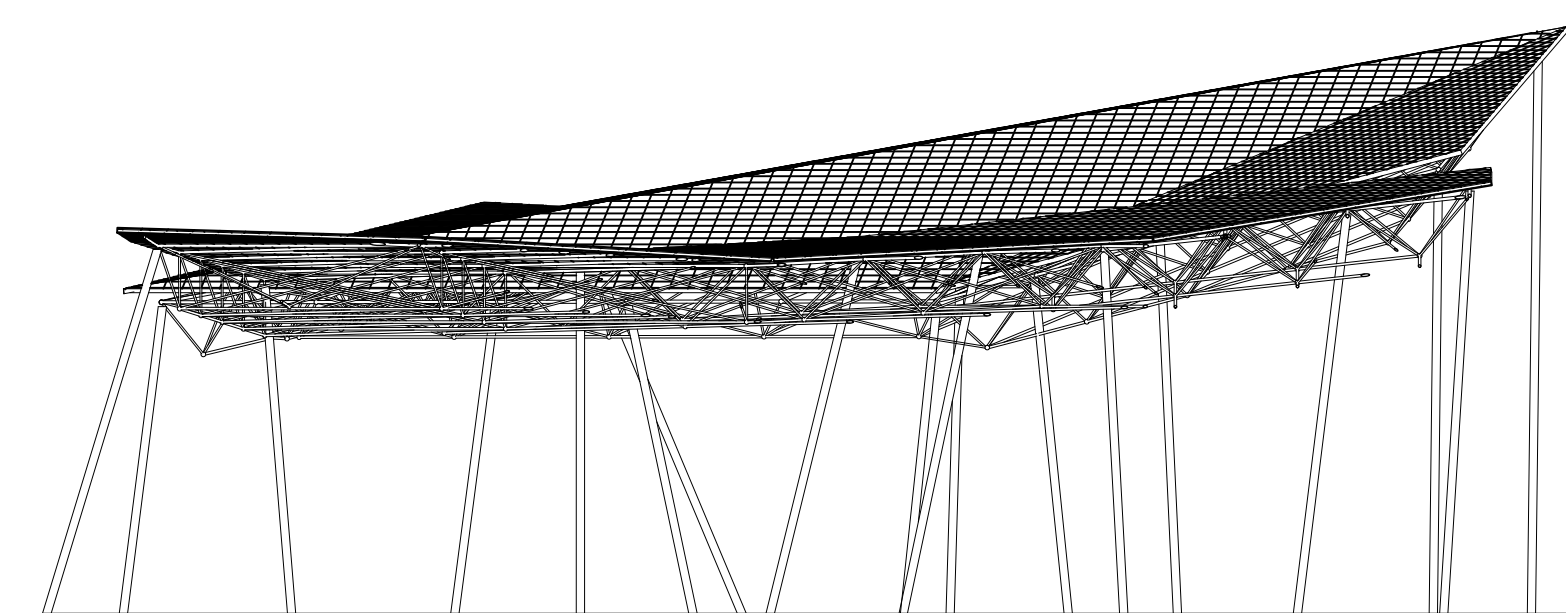

SECTION V3-V3


L Channel

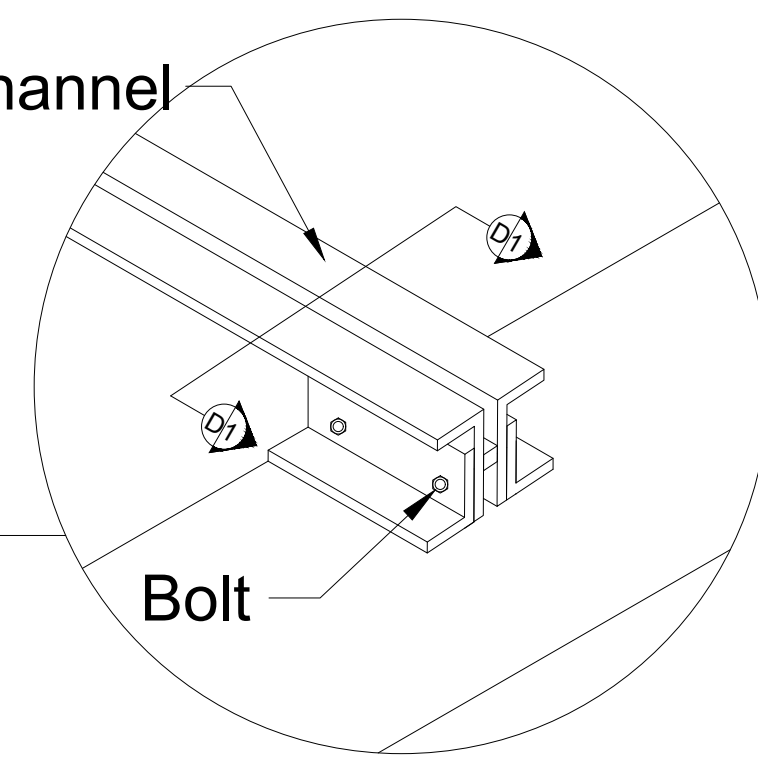

Detail 1 : JOIST CONNECTION TO TOP CHORD

Plate

Bolt

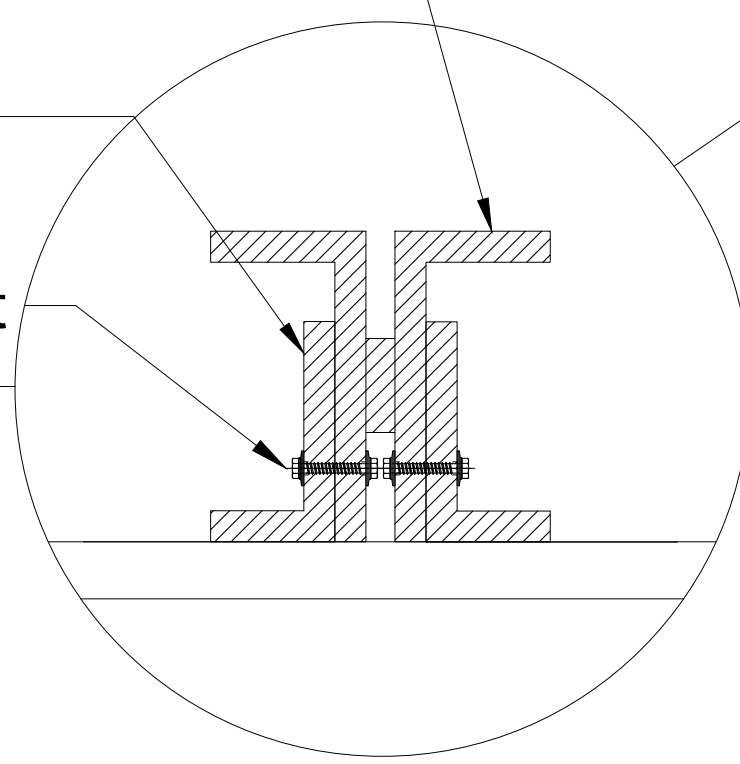

Section D1

L Channel

DEEP LONG SPAN JOIST (DLH JOIST)

0.55m

ALL TRUSS MEMBERS ARE WELDED

FLAT PRATT TRUSS

3m

TOP CHORD: HSS 350X20.
VERTICAL WEBS: HSS 300X15.
DIAGONAL WEBS: HSS 250X10.
TOP CHORD: HSS 350X20.

CABLE BOLTED TO ANCHOR

ANCHOR WELDED ON END PLATE

END PLATE WELDED ON BEAM

Turnbuckle

GALVANIZED STEEL CABLE

DETAIL 3: CABLE BRACING

DETAIL 2: CABLE ANCHOR

ISOLATED VIEW 2 : STEEL FRAME

STEEL COLOUMN
WELDED ON BASE PLATE

BOLTS

COLOUMN STIFFENER PLATE
BOLTED TO COLOUMN

GROUT

NECK COLOUMN

DETAIL 4: COLOUMN

ANCHOR BOLTS

COLOUMN STIFFENER PLATE
WELDED TO BASE PLATE

NODE SUPPORTER PLATE
STEEL BOLTED TO STIFFNER

STIFFNER WELDED TO
COLOUMN CAP

WELDED COLOUMN CAP

CHSS 500X50 STEEL COLOUMN

DETAIL 5: TOP CORD CONNECTION


BAR
HEAD
SLEEVE
NODE

HSS 10X8X3/8

HSS 500X50

S18x70

HSS 500X300X40

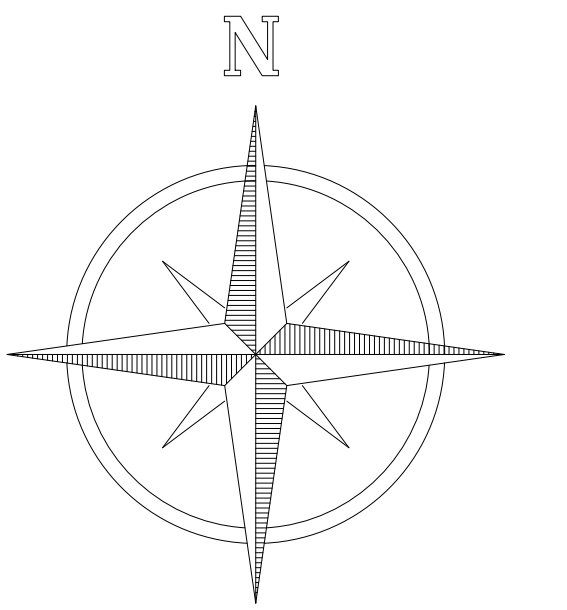

ALL UNITS IN METER

Design Studio (7), Technical
Project, 2024/2025

INSTRUCTORS:

Dr. Altayeb Qasem Co.
Prof. M. Essam Shaawat
Dr. Salah Alghamdi
Eng. Rehan Jamil
Eng. Waleed Alrushaidan

DONE BY:
ABDULELAH ALQABBANI

PROJECT:
MUSEUM

DRAWING NAME:
STRUCTURE DETAILS

SCALE:
...

SHEET NUMBER:
A19